


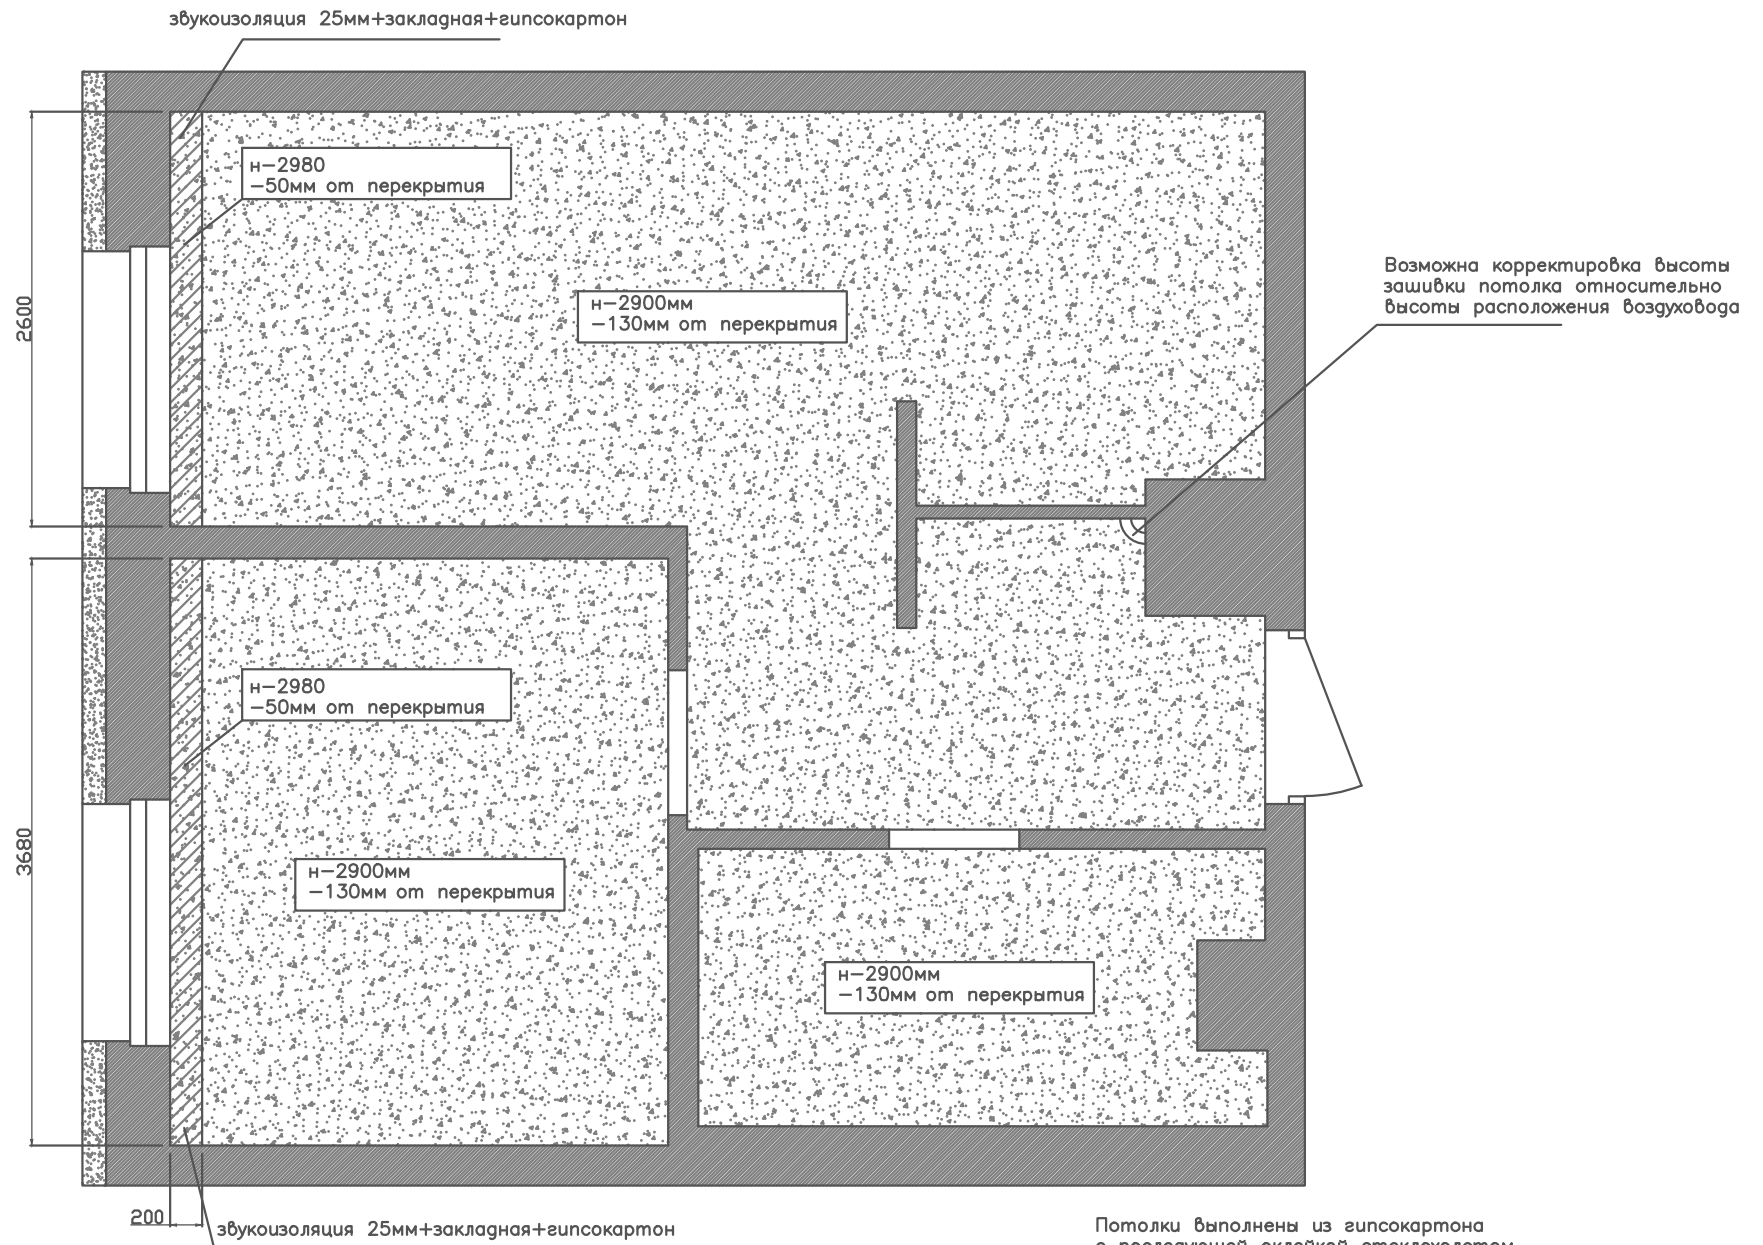

Потолки выполнены из гипсокартона с последующей оклейкой стеклохолстом или гладким флизелином, и окраской Ral 9010

— Звукоизоляция Роквул Акустик батс 25-50мм 41.36 м.кв.

— Закладная

		Подпись	Дата	Санкт-Петербург наб.Черной Речки 35 кв.453	
Заказчик	Данилова И.В.			Проект квартиры	Лист
Дизайнер	Коробейников Д.В.				Листов
План потолков					