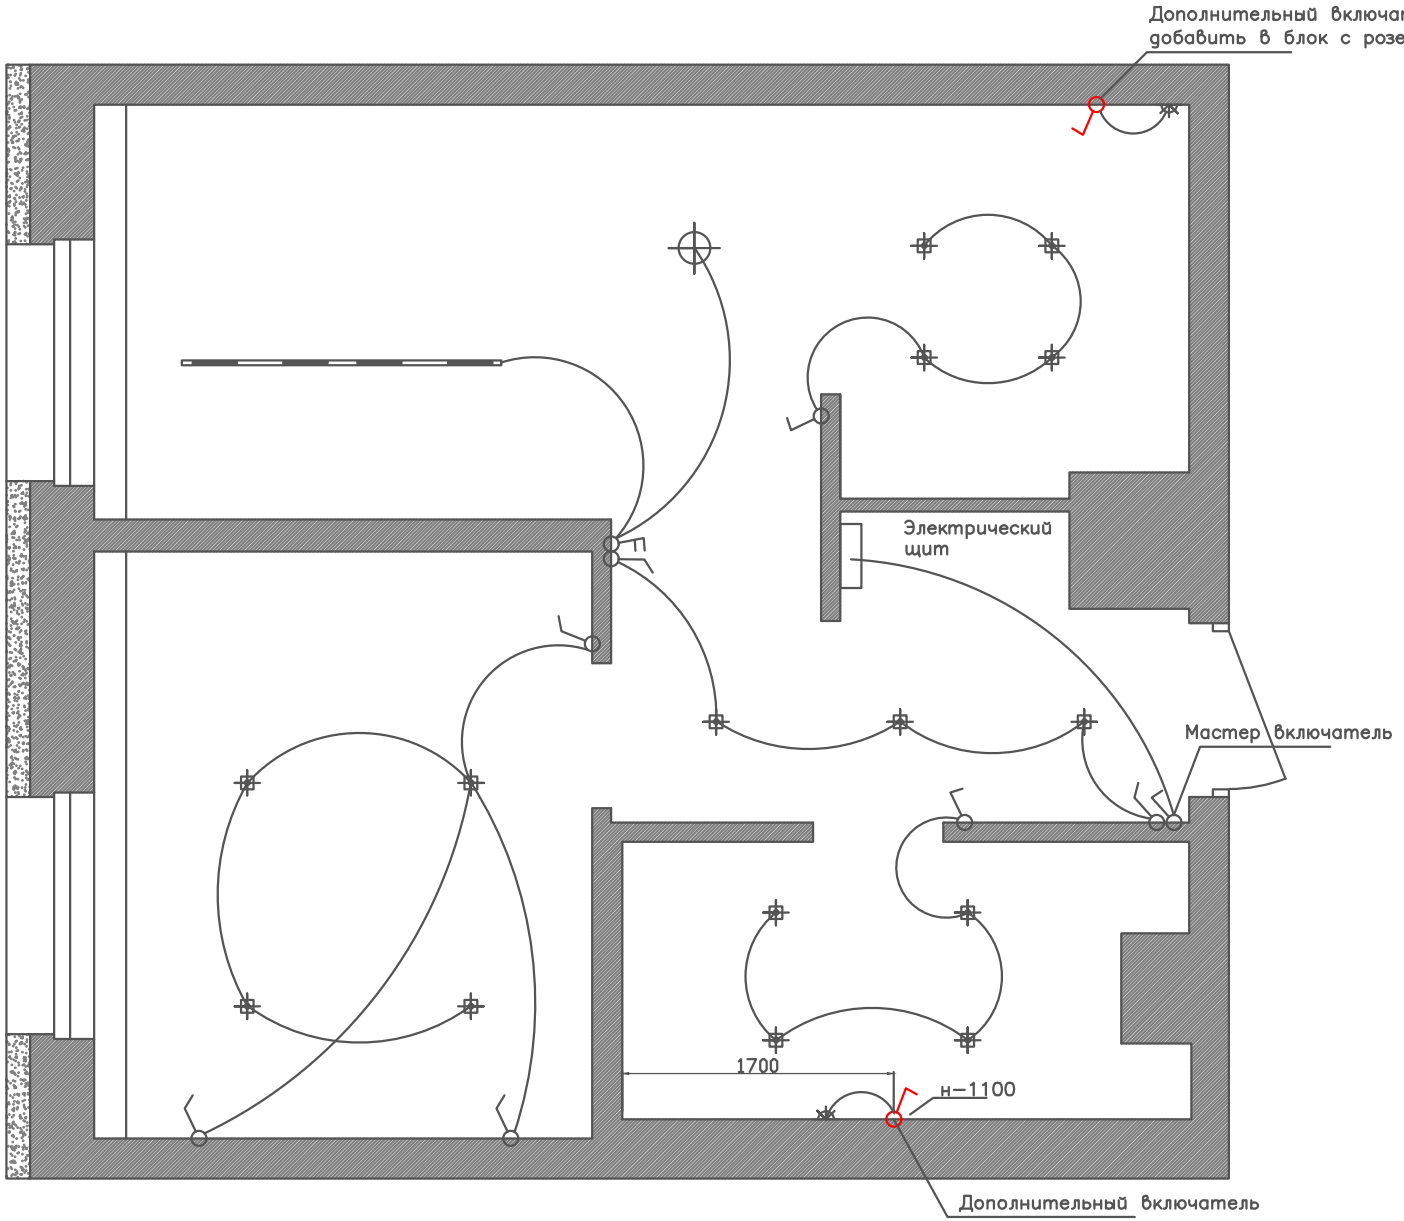


Переключатель двухклавишный

Переключатель одноклавишный

Выключатель одноклавишный

Выключатель двухклавишный

Все выключатели размещаются на высоте 900мм, и 150мм от края проема
Кроме ванных комнат Н-1100мм, или где указана высота

		Подпись	Дата	Санкт-Петербург наб.Черной Речки 35 кв.453		
Заказчик	Данилова И.В.			Проект квартиры	Лист	Листов
Дизайнер	Коробейников Д.В.					
				План установки выключателей по группам		