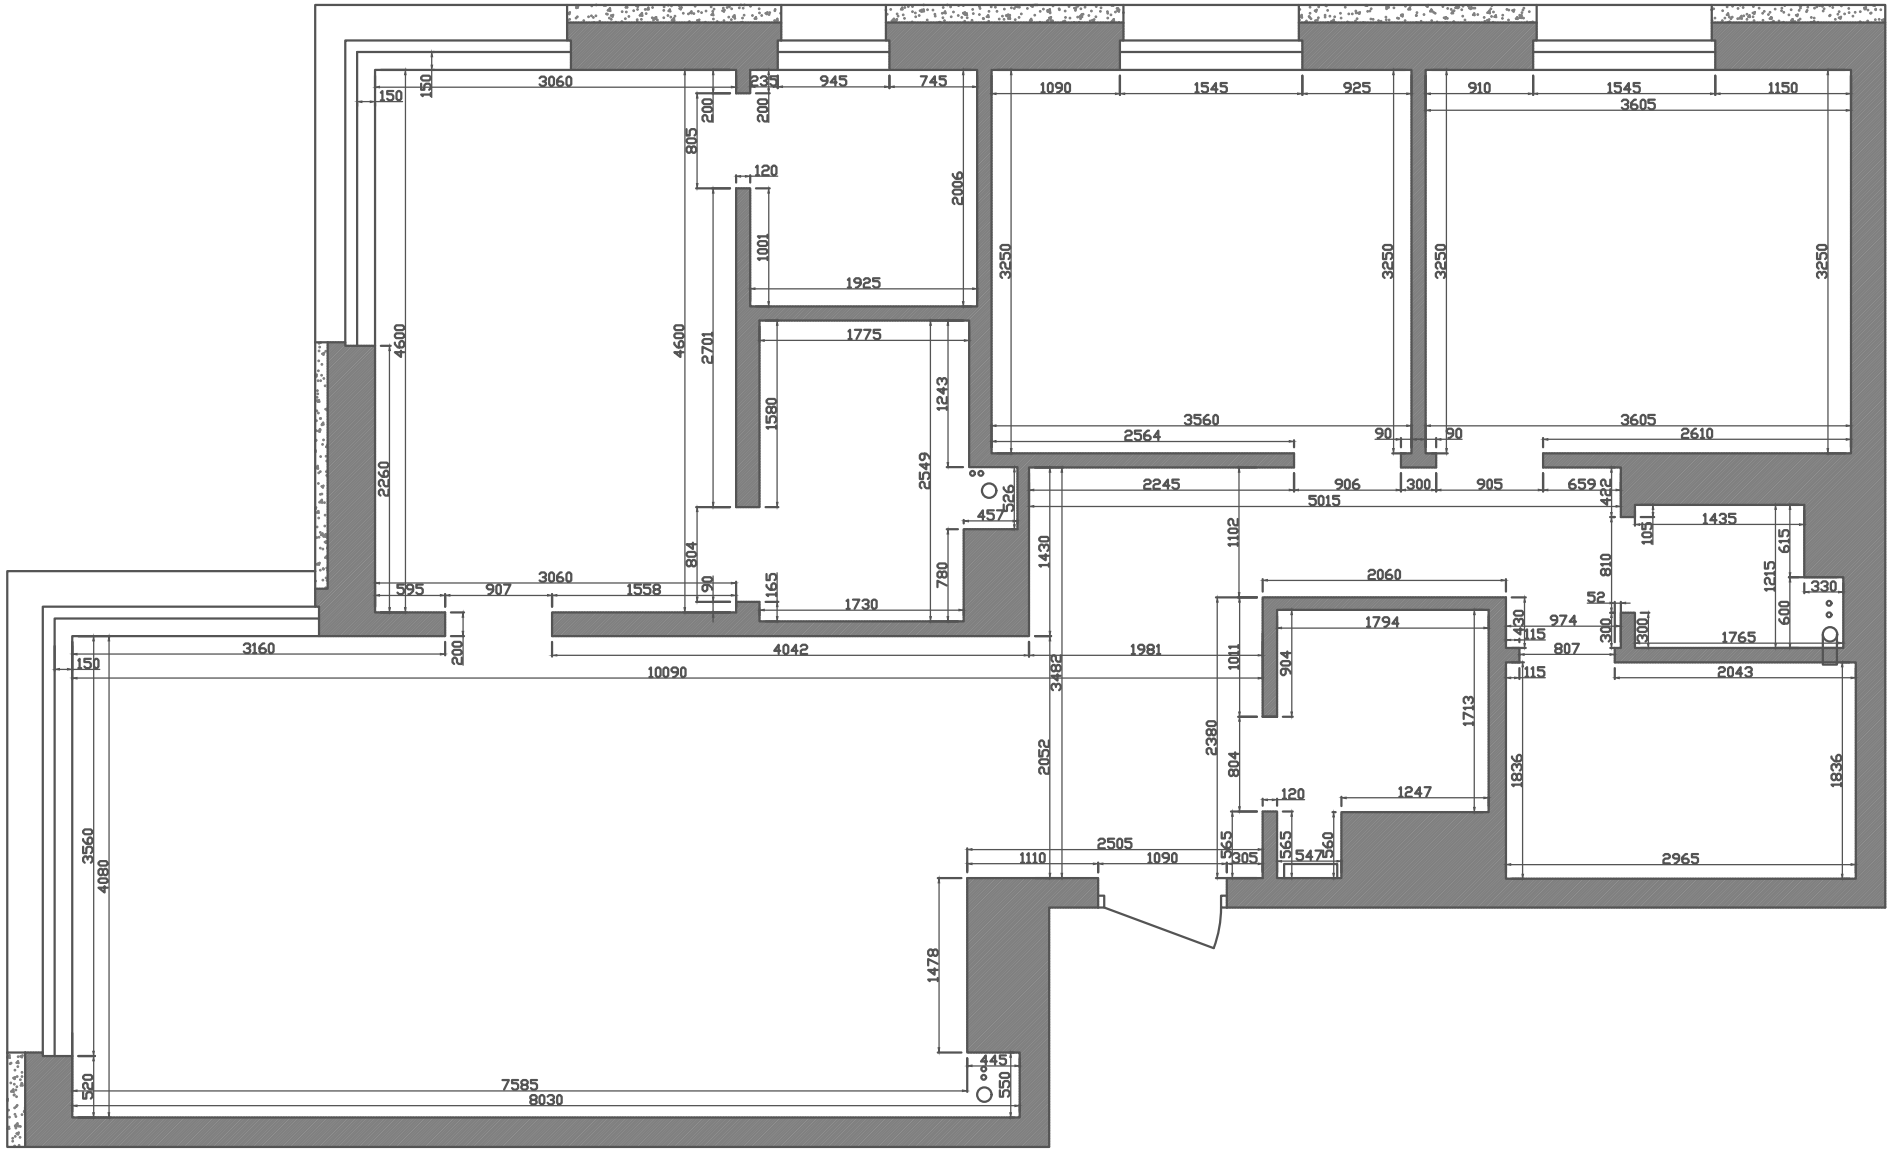


Площадь 101.93 м.кв.

| | | Подпись | Дата | Санкт–Петербург наб.Черной Речки 35 кв.25 | | |
|---|---|---|---|---|---|---|
| Заказчик | Данилова И.В. | | | Проект квартиры | Лист | Листов |
| Дизайнер | Коробейников Д.В. | | | | | |
| План размерный | | | | | | |