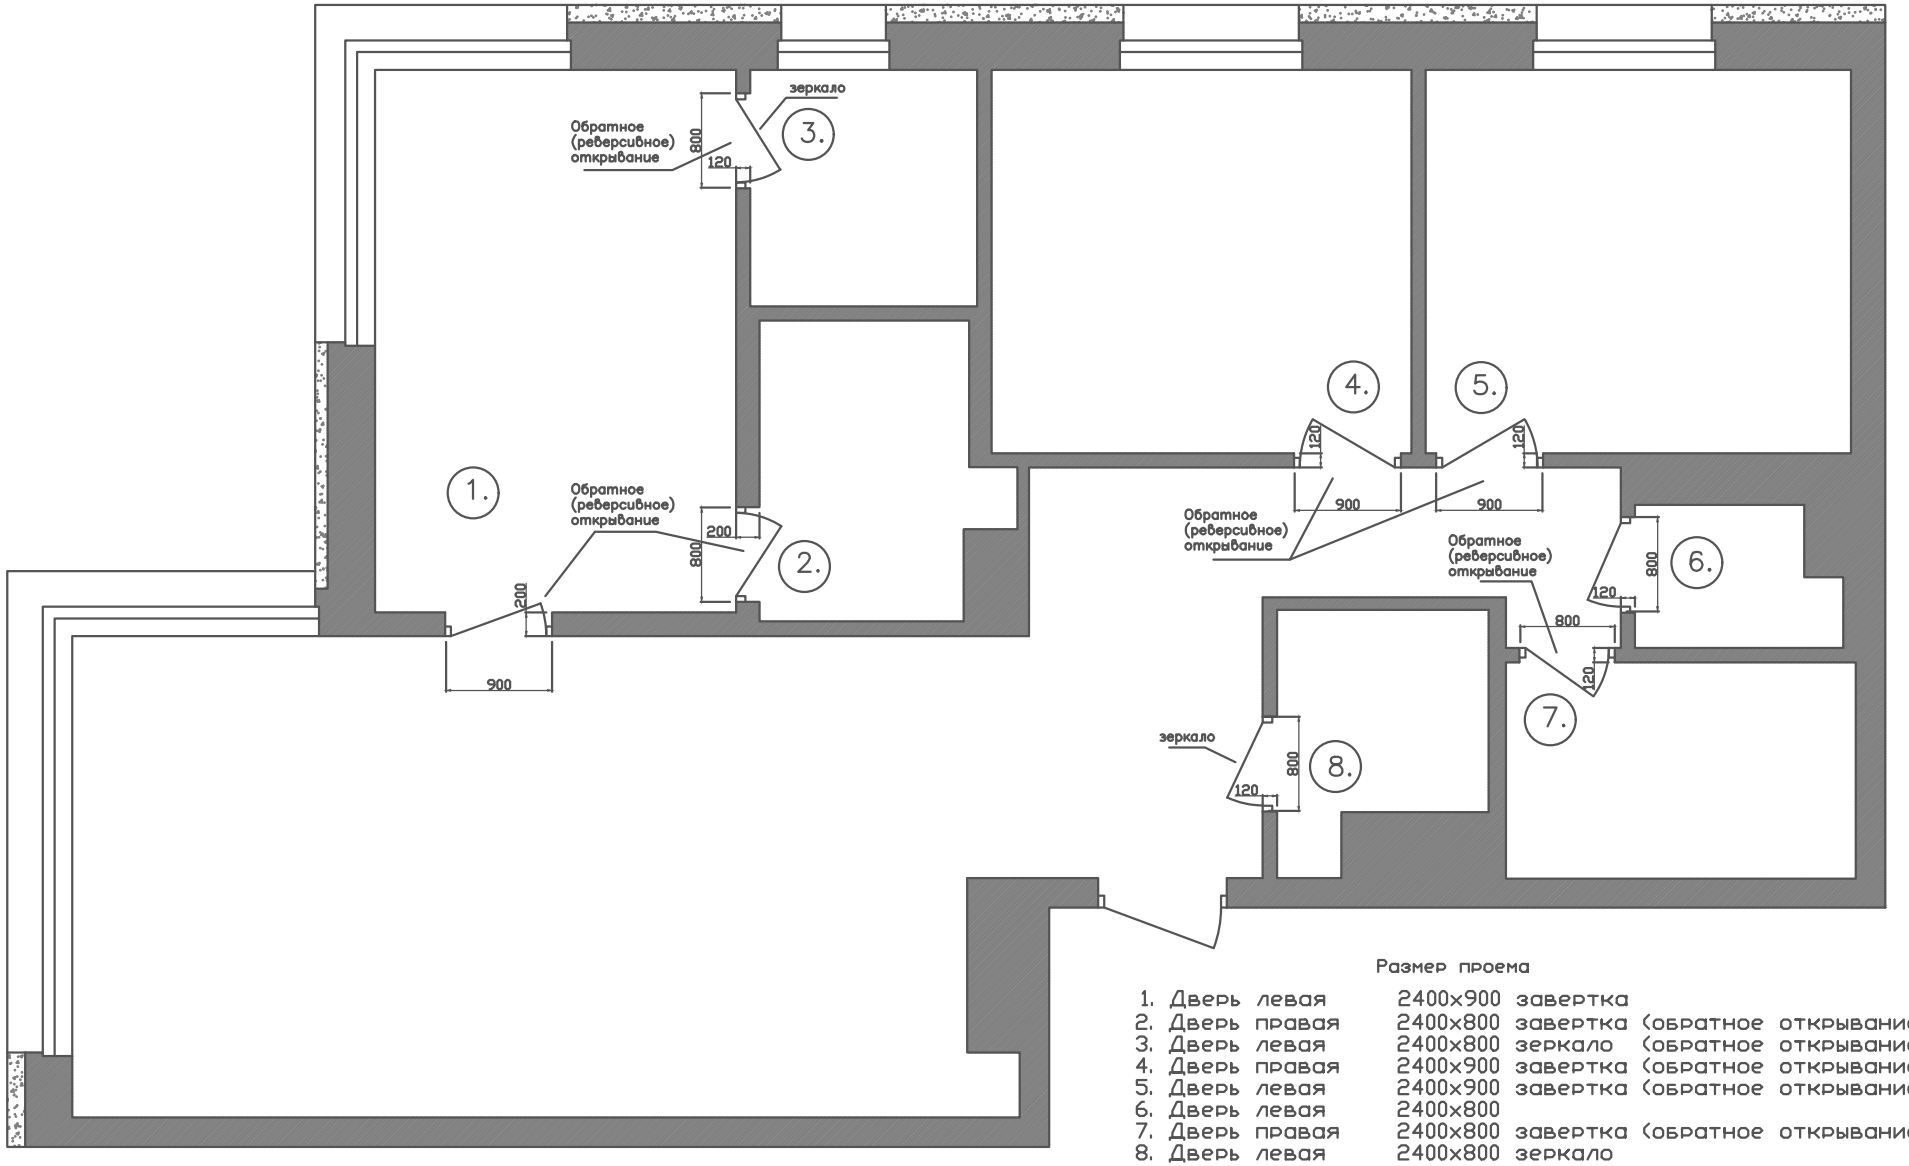


Размер проема

1.	Дверь левая	2400x900	завертка
2.	Дверь правая	2400x800	завертка (обратное открывание)
3.	Дверь левая	2400x800	зеркало (обратное открывание)
4.	Дверь правая	2400x900	завертка (обратное открывание)
5.	Дверь левая	2400x900	завертка (обратное открывание)
6.	Дверь левая	2400x800	
7.	Дверь правая	2400x800	завертка (обратное открывание)
8.	Дверь левая	2400x800	зеркало

Плинтус 82 м.п.

		Подпись	Дата	Санкт–Петербург наб.Черной Речки 35 кв.25	
Заказчик	Данилова И.В.				
Дизайнер	Коробейников Д.В.			Проект квартиры	Лист / Листов
План открывания дверей. Ведомость проемов					