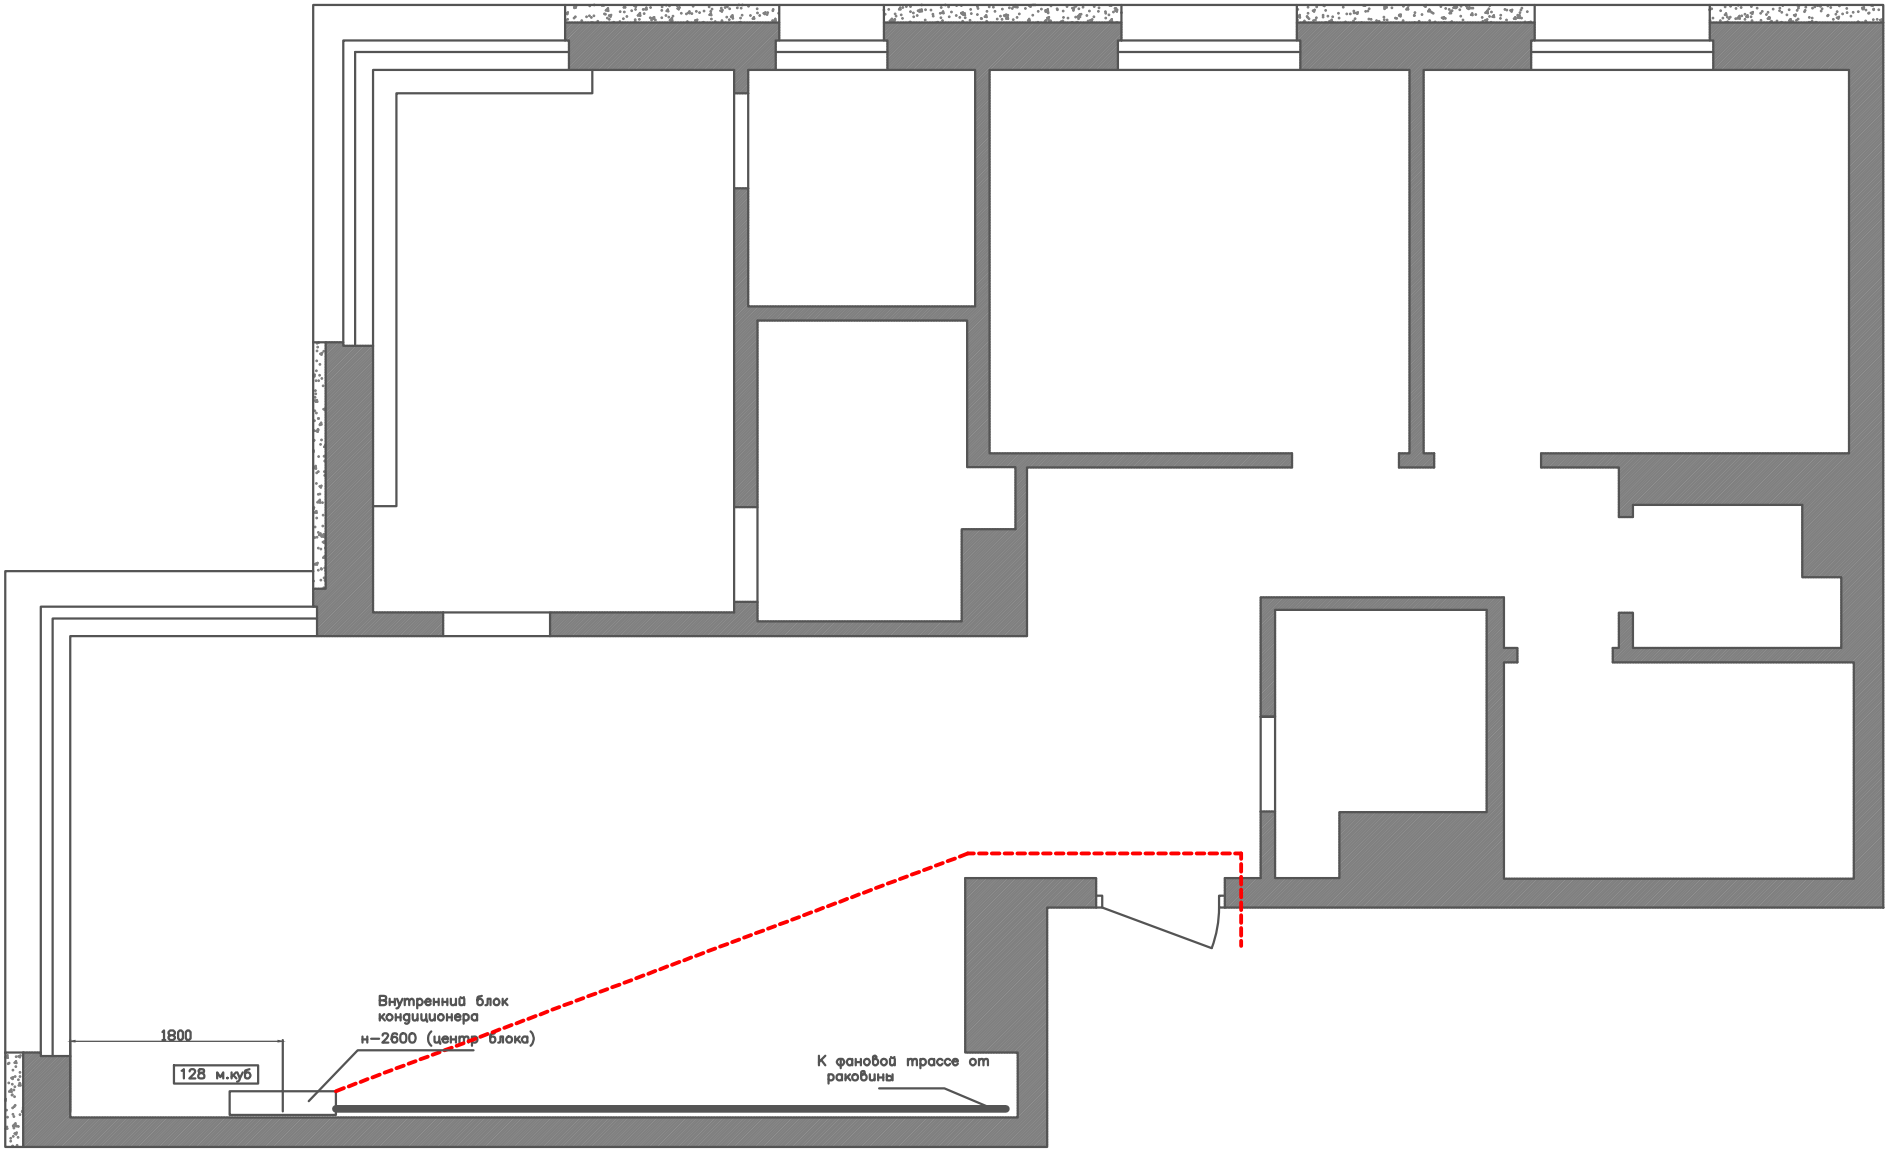

Фреоновая трасса 10 м.п.

Дренаж для конденсата 8 м.п.

Трассы заштробить в стены

		Подпись	Дата	Санкт–Петербург наб.Черной Речки 35 кв.25		
Заказчик	Данилова И.В.			Проект квартиры	Лист	Листов
Дизайнер	Коробейников Д.В.					
План монтажа кондиционеров. Фреоновые трассы						