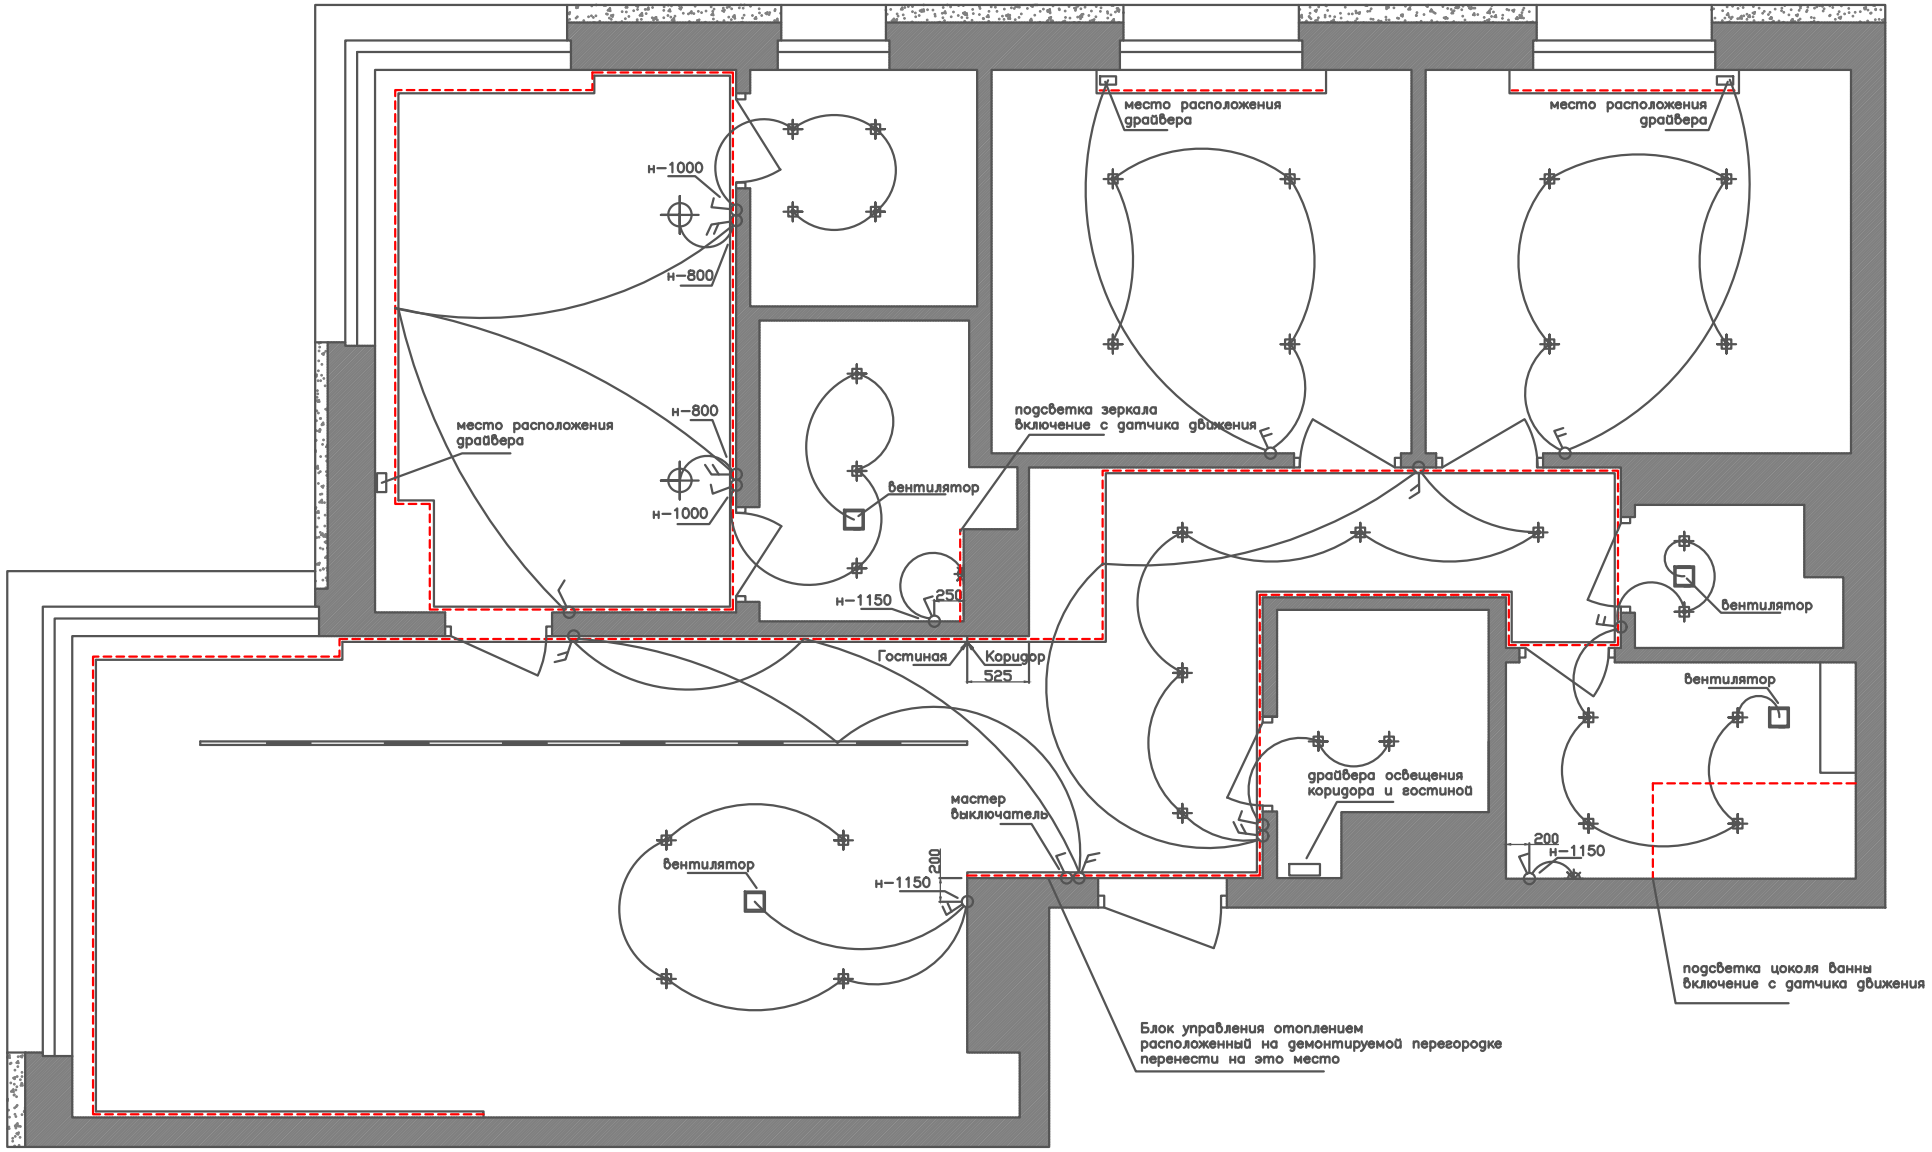

Переключатель двухклавишный

Переключатель одноклавишный

Выключатель одноклавишный

Выключатель двухклавишный

Все выключатели размещаются на высоте 1000мм, и 150мм от края проема
Кроме ванных комнат Н–1150мм, или где указана высота

		Подпись	Дата	Санкт–Петербург наб.Черной Речки 35 кв.25		
Заказчик	Данилова И.В.			Проект квартиры	Лист	Листов
Дизайнер	Коробейников Д.В.					
				План установки выключателей по группам		