


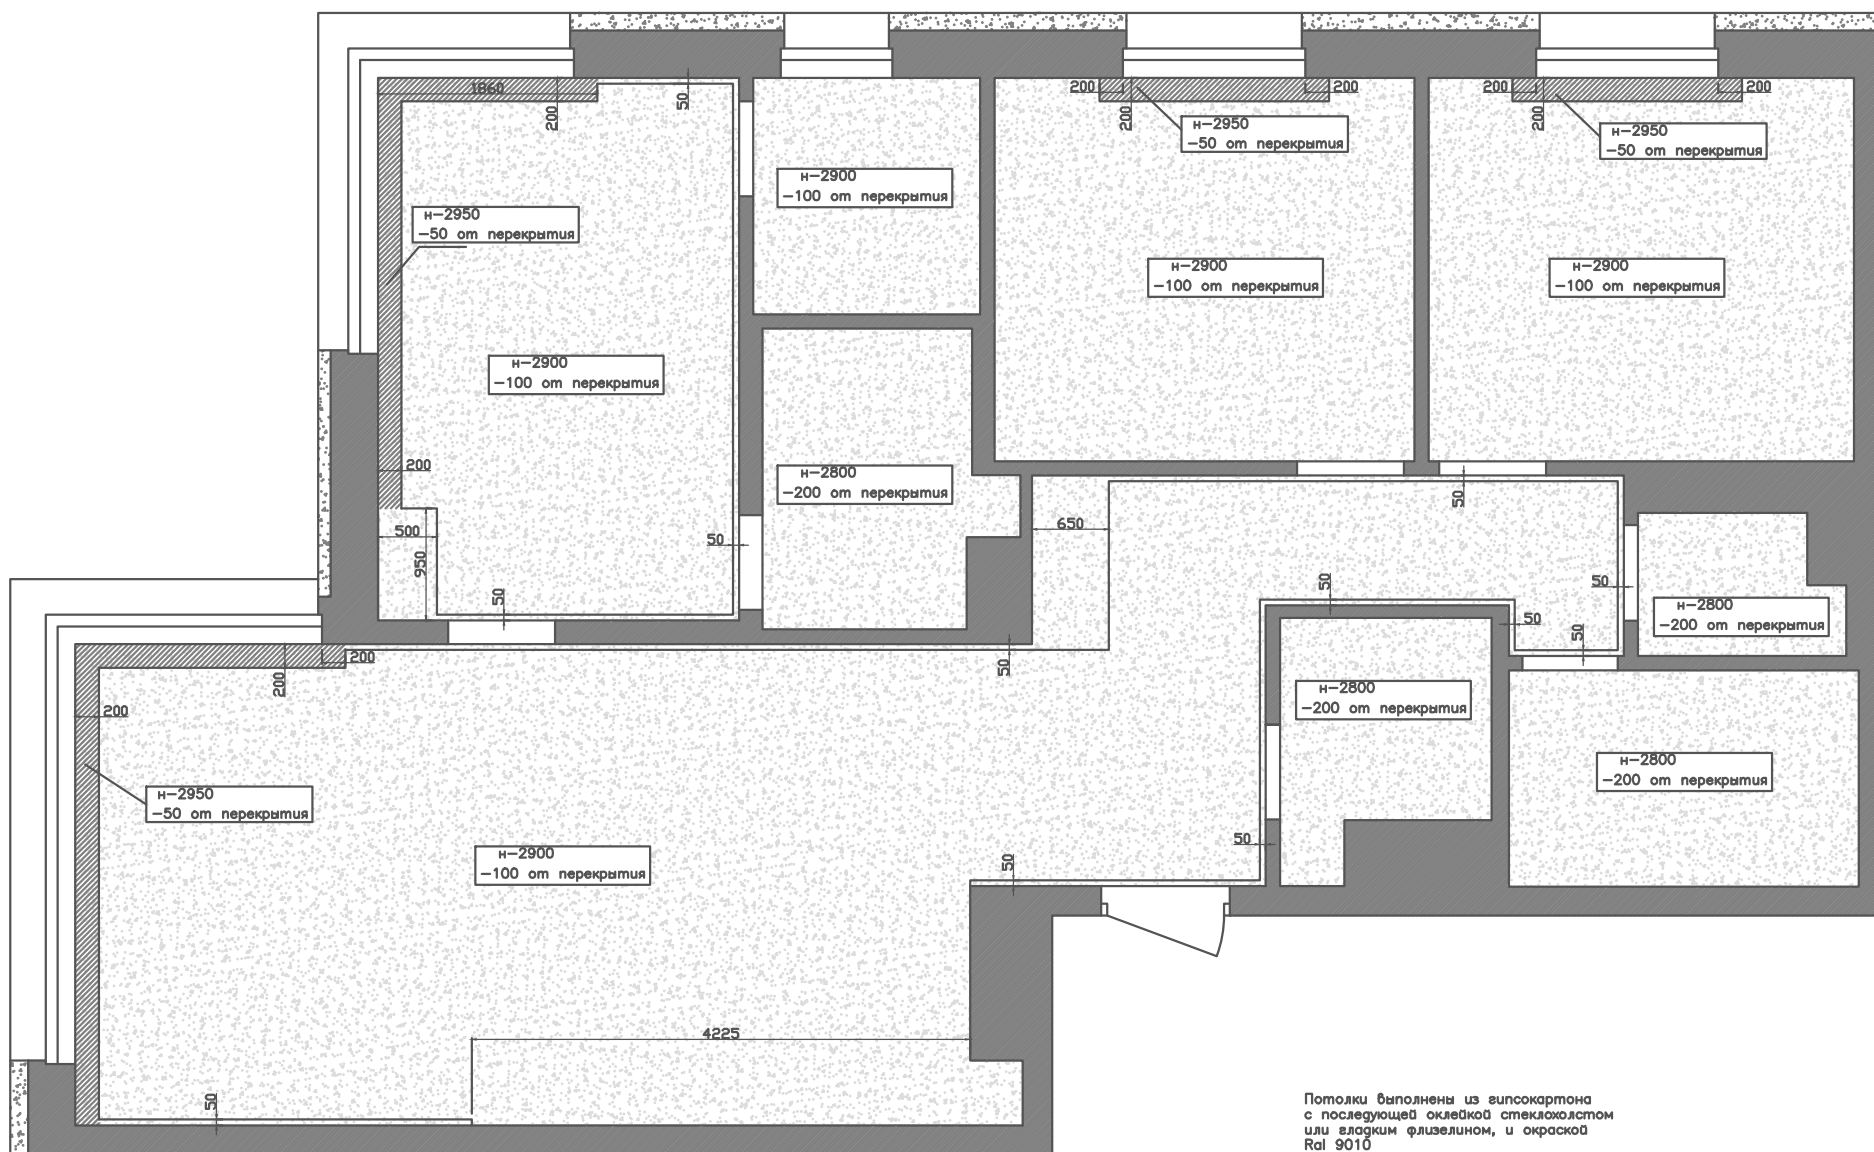

—Звукоизоляция Роквул Акустик батс 25—50мм 102 м.кв.

—Закладная

Потолки выполнены из гипсокартона
с последующей оклейкой стеклохолстом
или гладким флизелином, и окраской
Ral 9010

		Подпись	Дата	Санкт-Петербург наб.Черной Речки 35 кв.25	
Заказчик	Данилова И.В.			Проект квартиры	Лист
Дизайнер	Коробейников Д.В.				Листов

План потолков