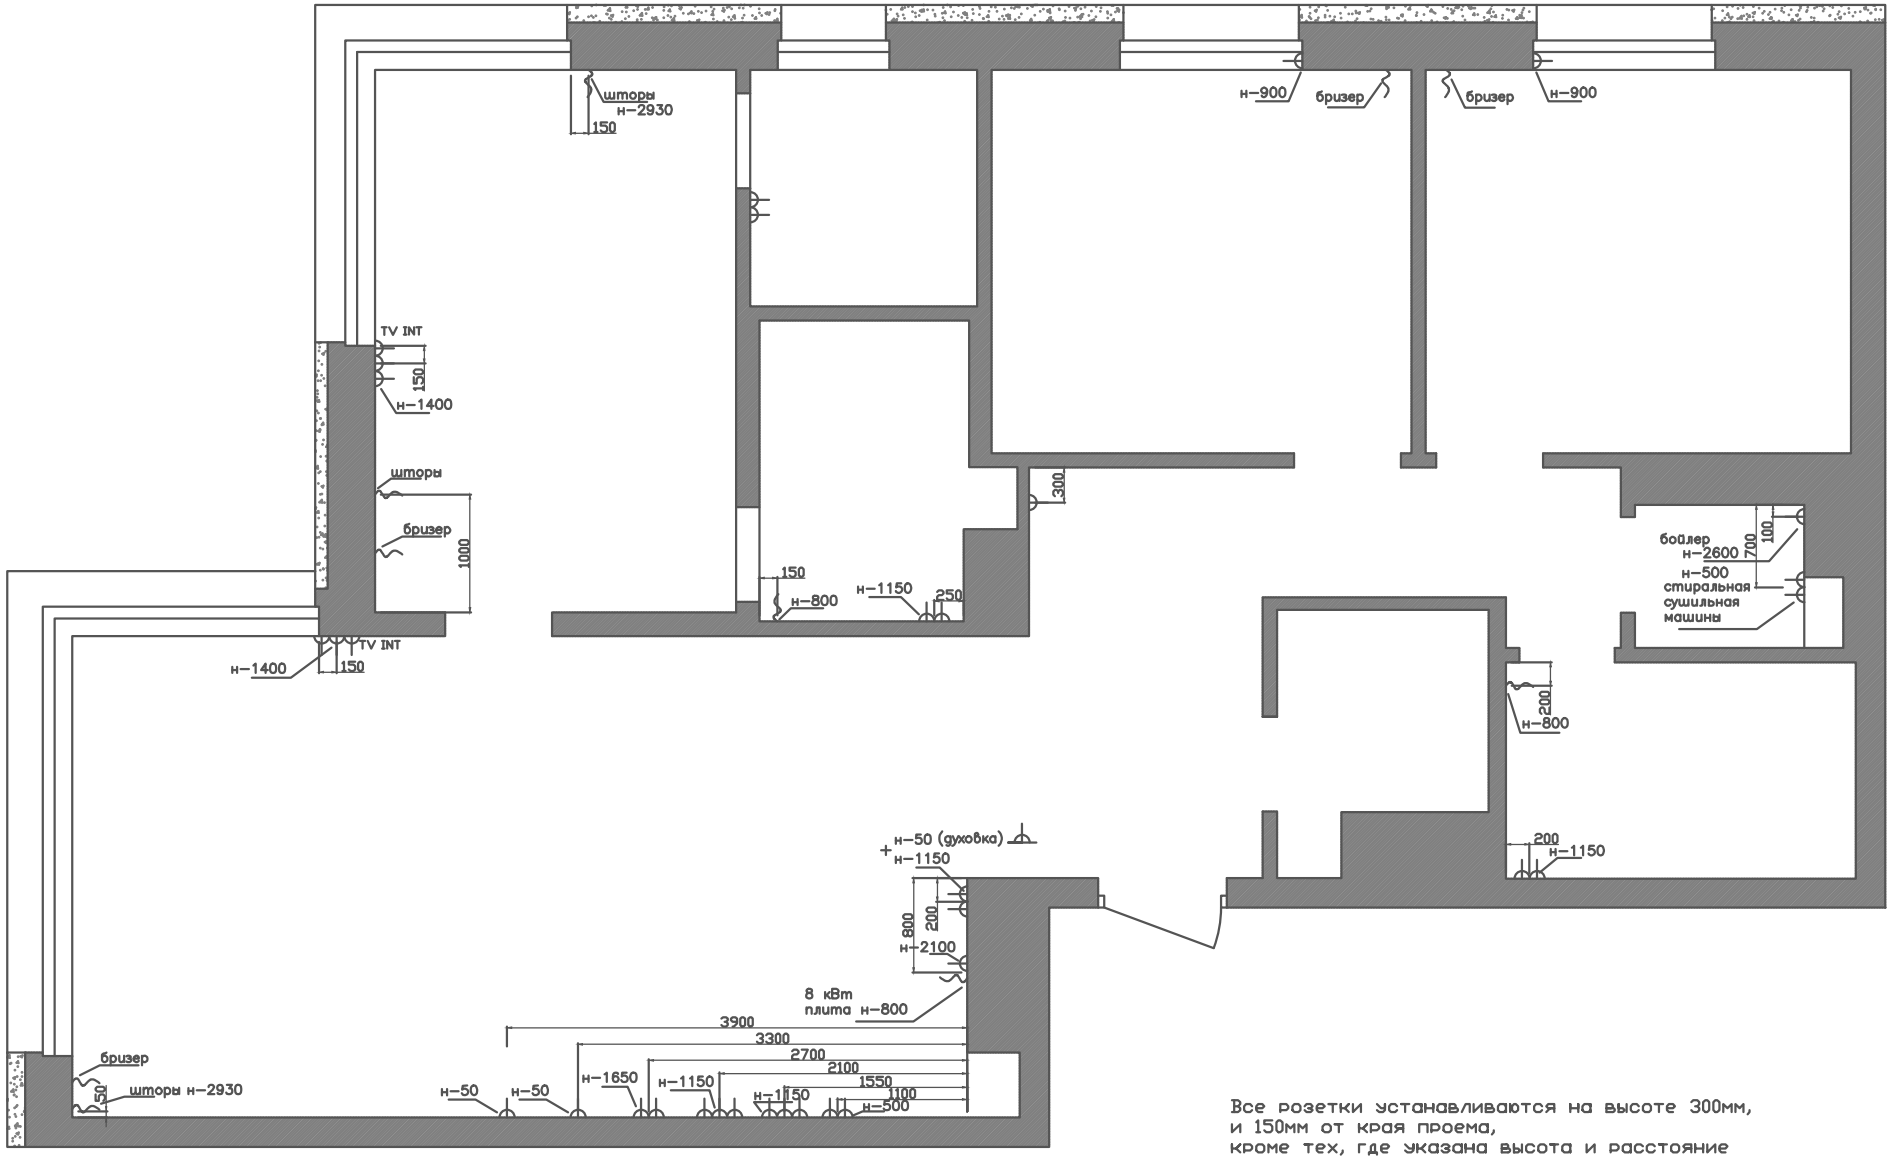

Все розетки устанавливаются на высоте 300мм,
и 150мм от края проема,
кроме тех, где указана высота и расстояние

⏚ — Электрическая розетка
TV — Телевизионная розетка
INT — Интернет розетка
⌇ — Вывод провода 220в

		Подпись	Дата	Санкт–Петербург наб.Черной Речки 35 кв.25		
Заказчик	Данилова И.В.			Проект квартиры	Лист	Листов
Дизайнер	Коробейников Д.В.					
План установки дополнительных электрических розеток						