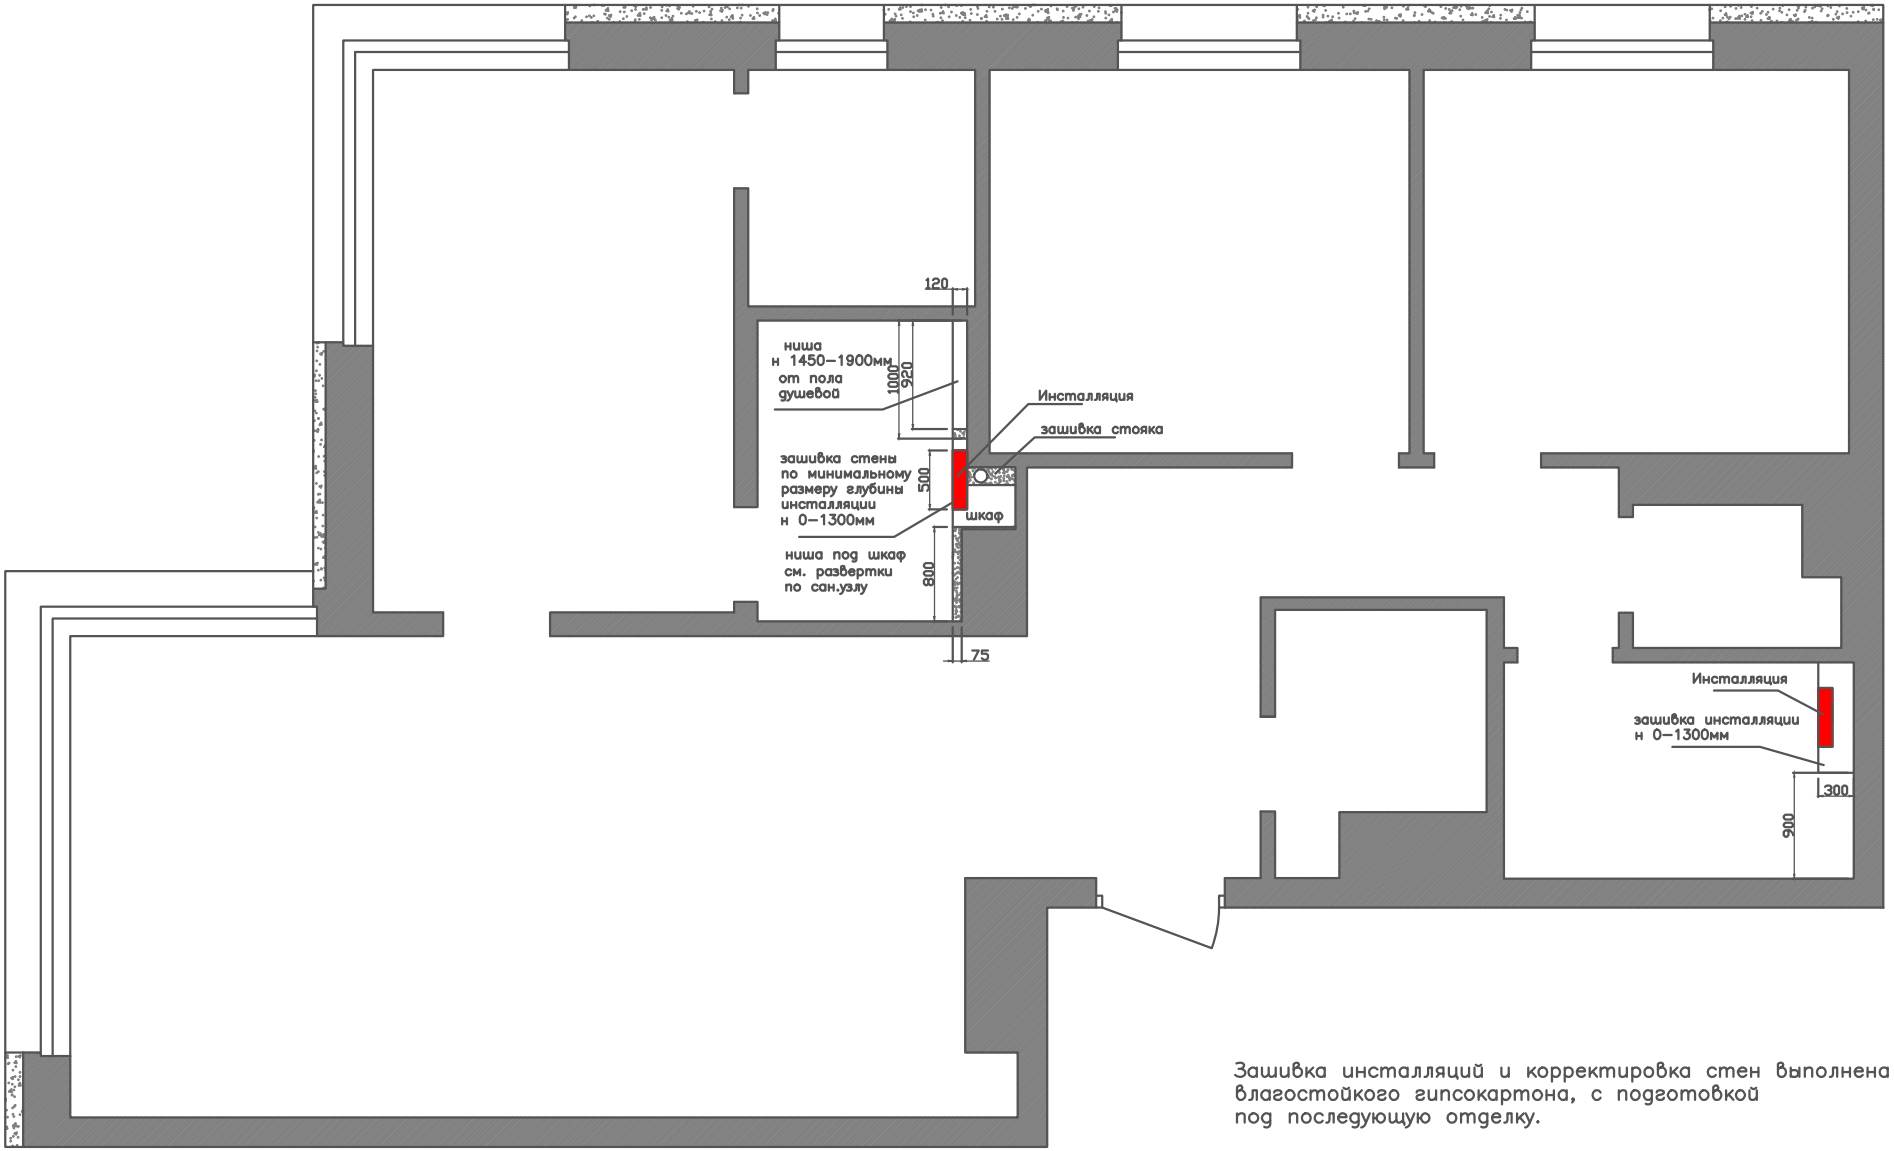


Зашивка инсталляций и корректировка стен выполнена из влагостойкого гипсокартона, с подготовкой под последующую отделку.

		Подпись	Дата	Санкт–Петербург наб.Черной Речки 35 кв.25		
Заказчик	Данилова И.В.			Проект квартиры	Лист	Листов
Дизайнер	Коробейников Д.В.					
План монтажа перегородок						