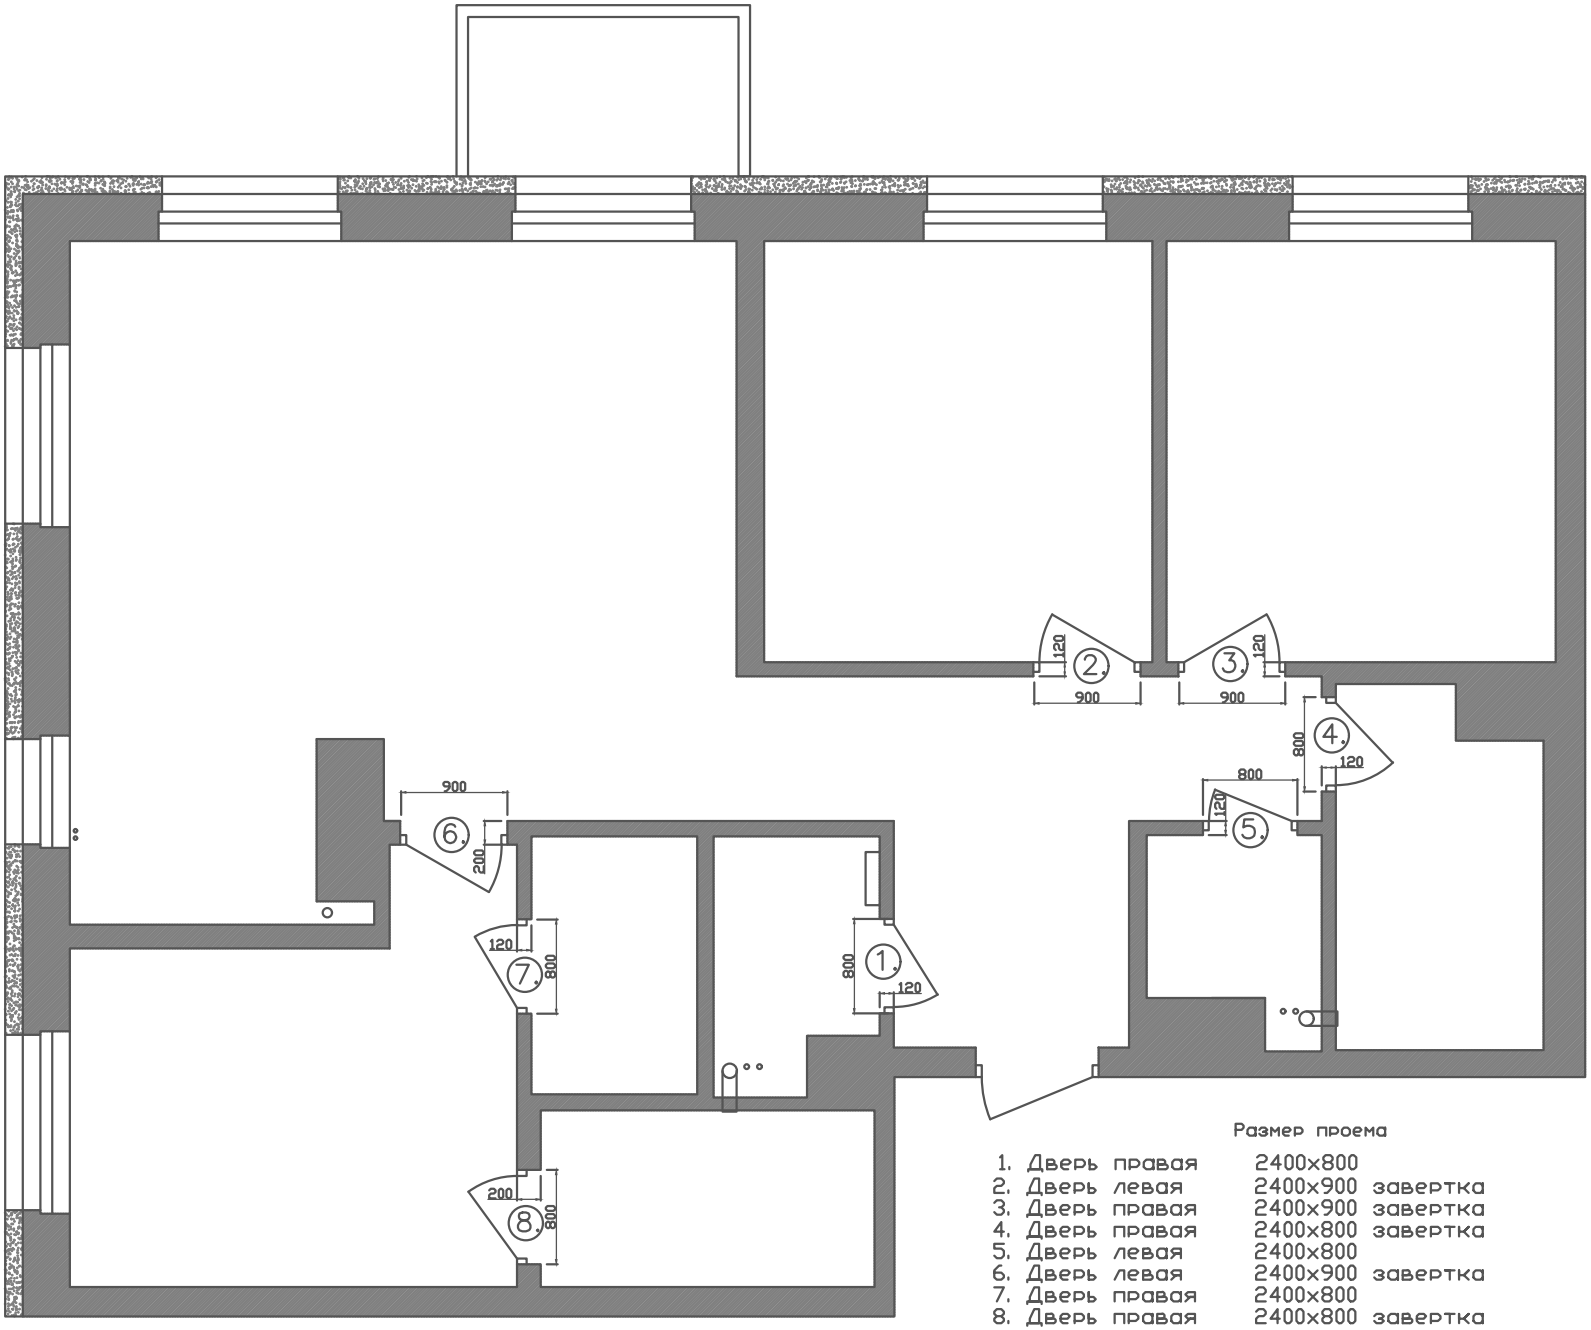

Размер проема

1.	Дверь правая	2400x800
2.	Дверь левая	2400x900 завертка
3.	Дверь правая	2400x900 завертка
4.	Дверь правая	2400x800 завертка
5.	Дверь левая	2400x800
6.	Дверь левая	2400x900 завертка
7.	Дверь правая	2400x800
8.	Дверь правая	2400x800 завертка

Плинтус – 80 м.п.

Плинтуса устанавливаются везде, кроме сан.узлов.

		Подпись	Дата	Санкт–Петербург наб.Черной Речки 35 кв.22		
Заказчик	Данилова И.В.			Проект квартиры	Лист	Листов
Дизайнер	Коробейников Д.В.					
План открывания дверей. Ведомость проемов						