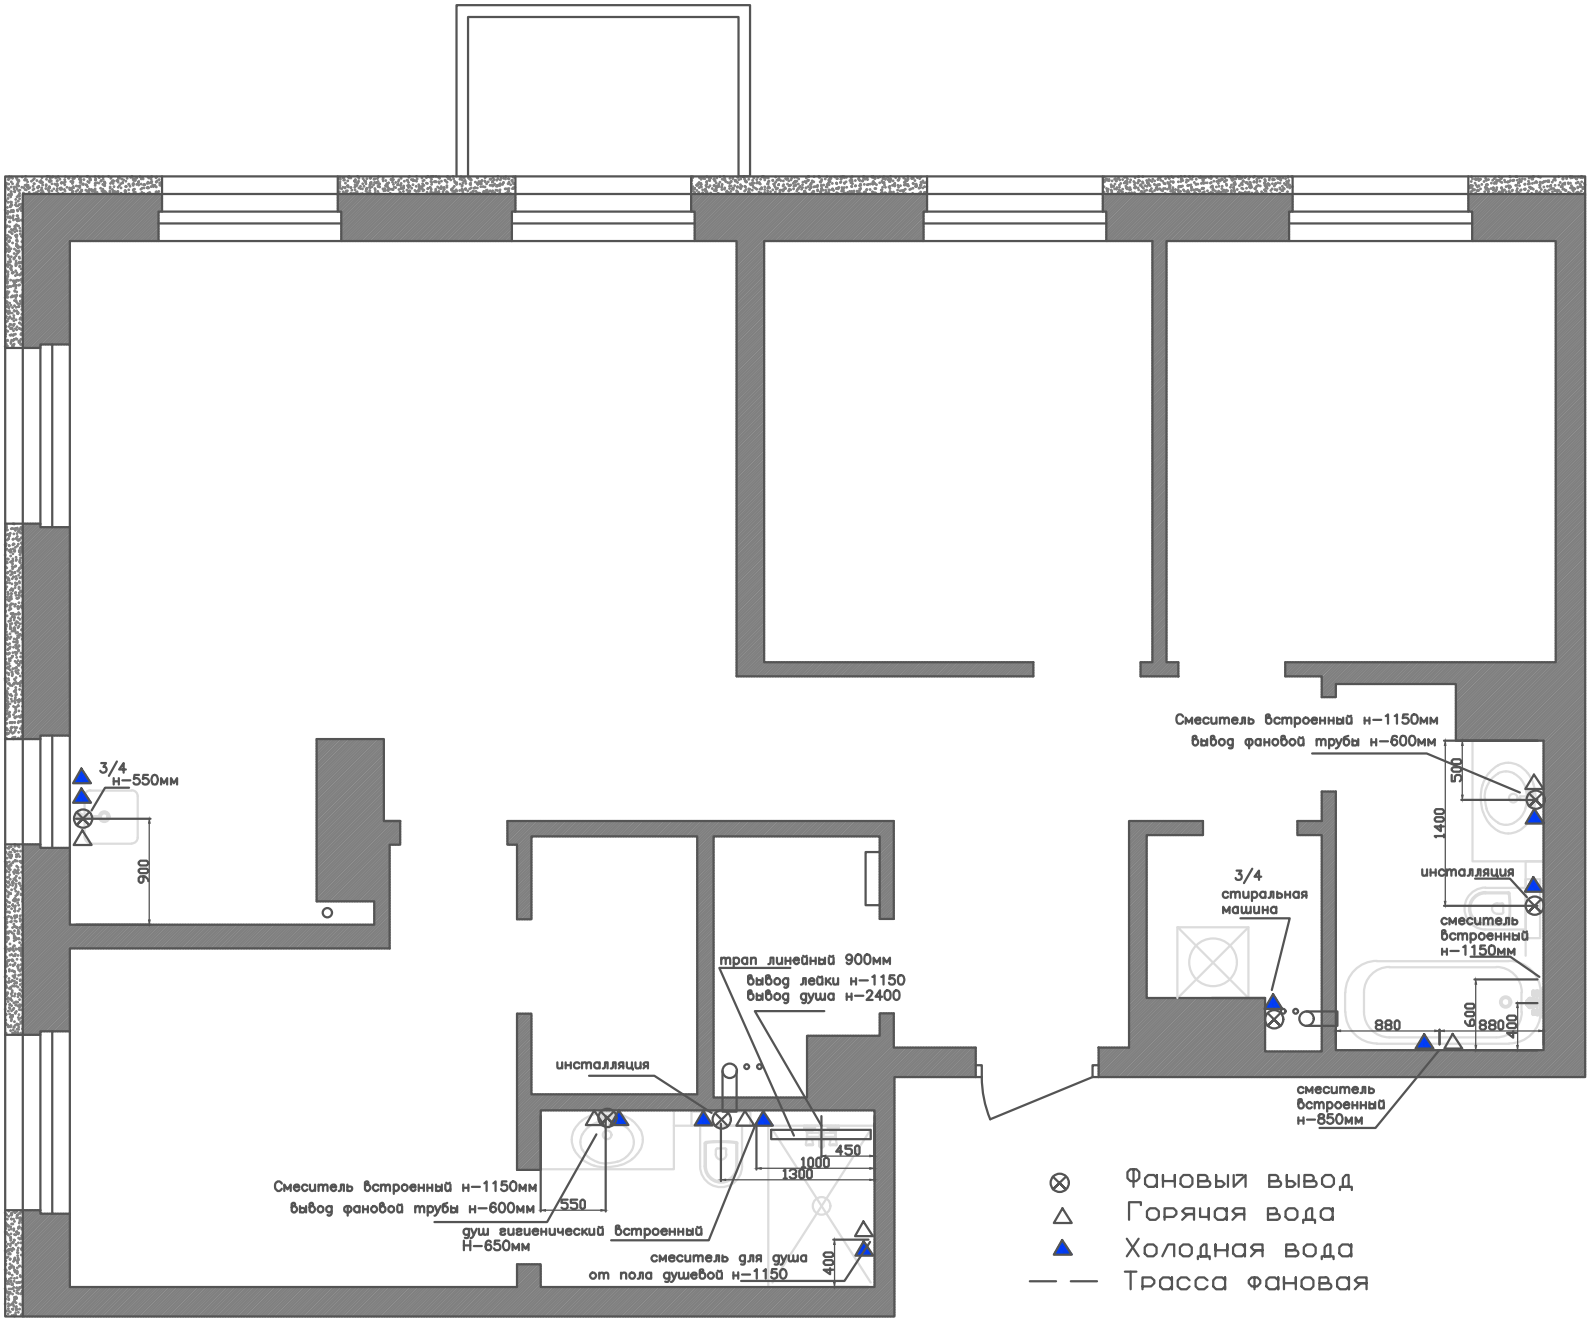


Все фановые выводы 50мм,
кроме инсталляции 110мм.
и стиральной машины 32мм.

Все водородетки 1/2, кроме тех,
где указан размер.

		Подпись	Дата	Санкт–Петербург наб.Черной Речки 35 кв.22		
Заказчик	Данилова И.В.			Проект квартиры	Лист	Листов
Дизайнер	Коробейников Д.В.					
План водоснабжения и канализации						