


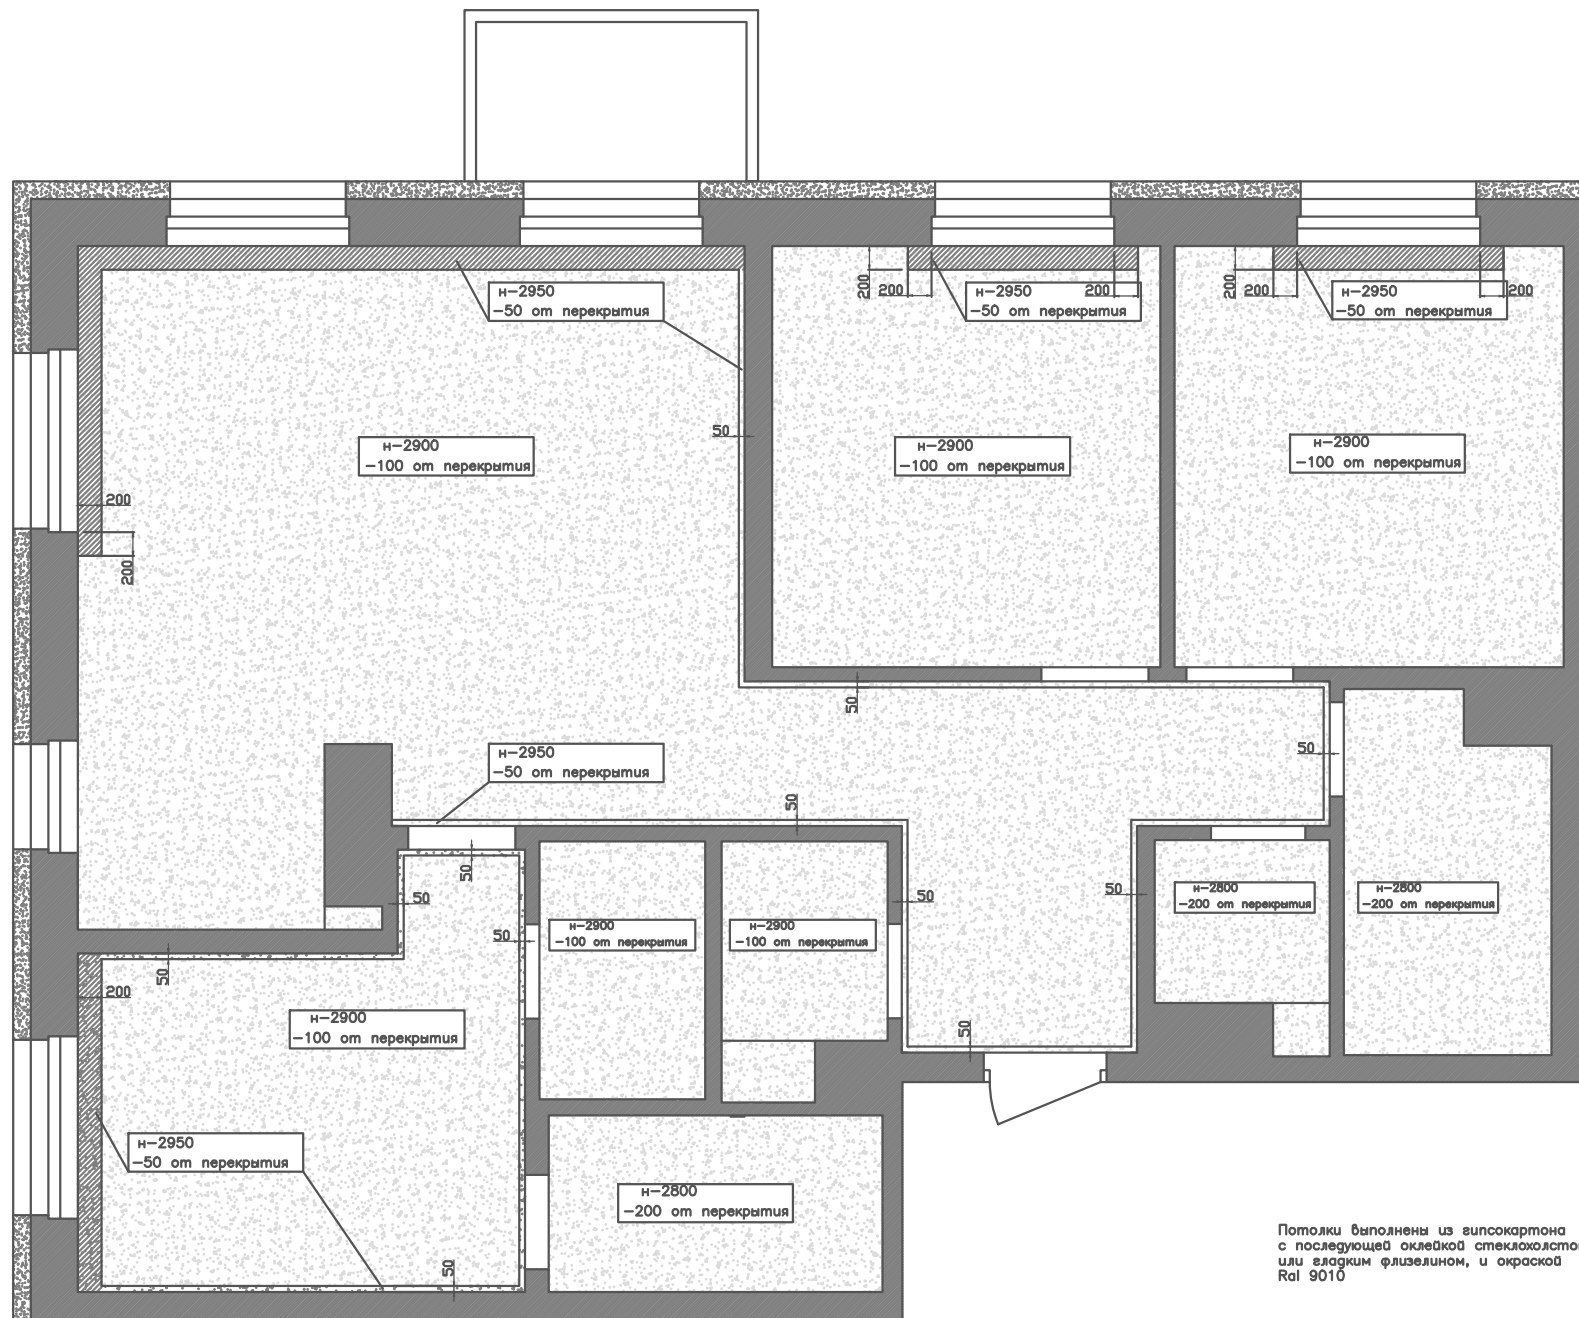

Звукоизоляция Роквул Акустик батс 25-50мм 93 м.кв.

Закладная

Заказчик	Данилова И.В.	Подпись	Дата	Санкт-Петербург наб.Черной Речки 35 кв.22		
Дизайнер	Коробейников Д.В.			Проект квартиры		Лист
План потолка				Листов		