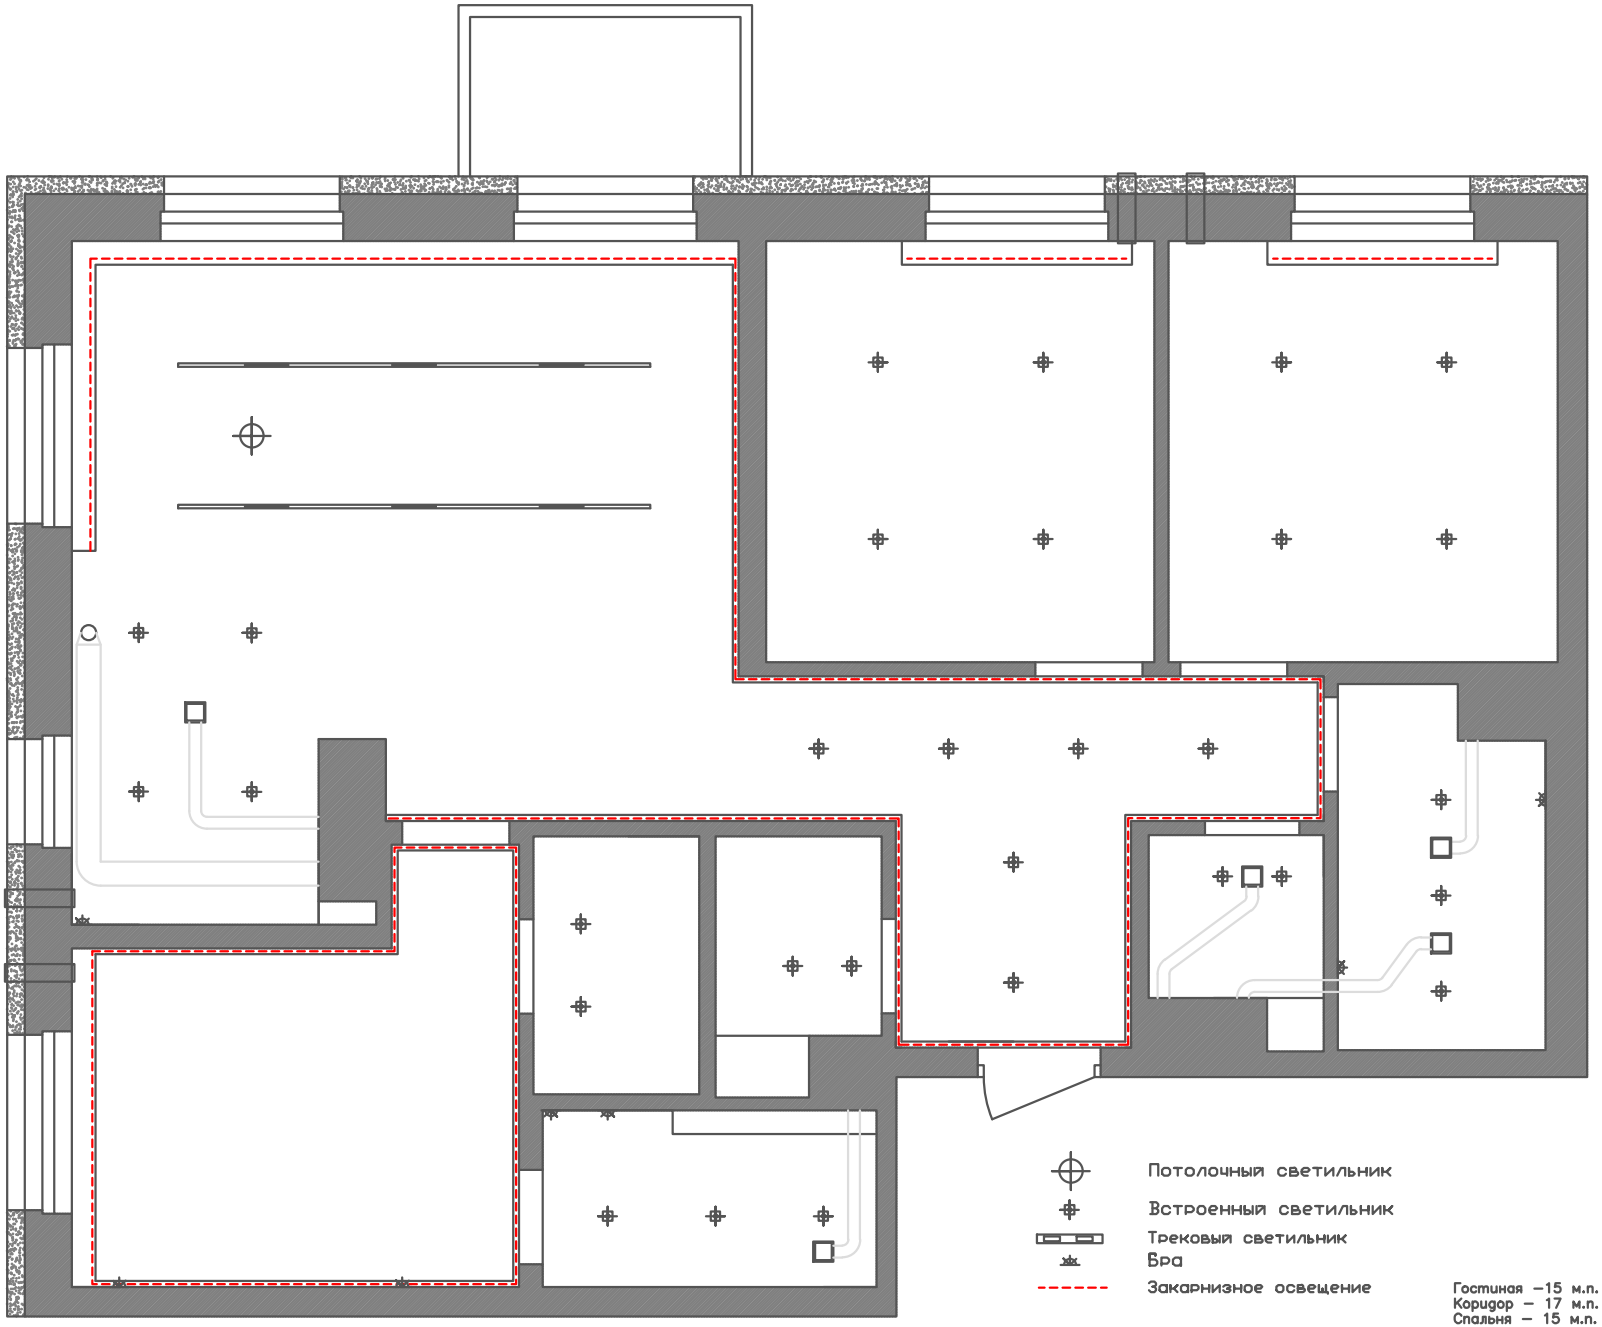


		Подпись	Дата	Санкт–Петербург наб.Черной Речки 35 кв.22		
Заказчик	Данилова И.В.			Проект квартиры	Лист	Листов
Дизайнер	Коробейников Д.В.					
План вентиляции совмещенный с планом освещения						